

www.prefabbricatimoioioli.it



COPERTURA BACACIER



Via F.lli Kennedy 24 Bagnatica (BG) - Tel: 035 681239
info@prefabbricatimoioioli.it



SISTEMA COPERTURA BACACIER

Il Sistema **Bacacier** è la risposta Moioli per edifici logistici a grande luce libera. Il sistema Bacacier permette di ridurre al minimo i pilastri interni, massimizzando la flessibilità degli spazi. La struttura si compone di pilastri, travi principali a I, arcarecci e canali in c.a.p., con copertura in lamiera grecata integrabile con isolamento, lucernari e impianti fotovoltaici.


Caratteristiche principali:

- Luci libere maglia strutturale in funzione delle necessità
- Numero ridotto di pilastri interni
- Resistenza al fuoco R90' – R120' – R180'
- Nodi e vincoli sismici certificati
- Compatibile con fotovoltaico e lucernari

Il sistema include:


- Pilastri in c.a.v.
- Travi centrali a "I" e travi a "U" laterali
- Arcarecci precompressi

STRUTTURA

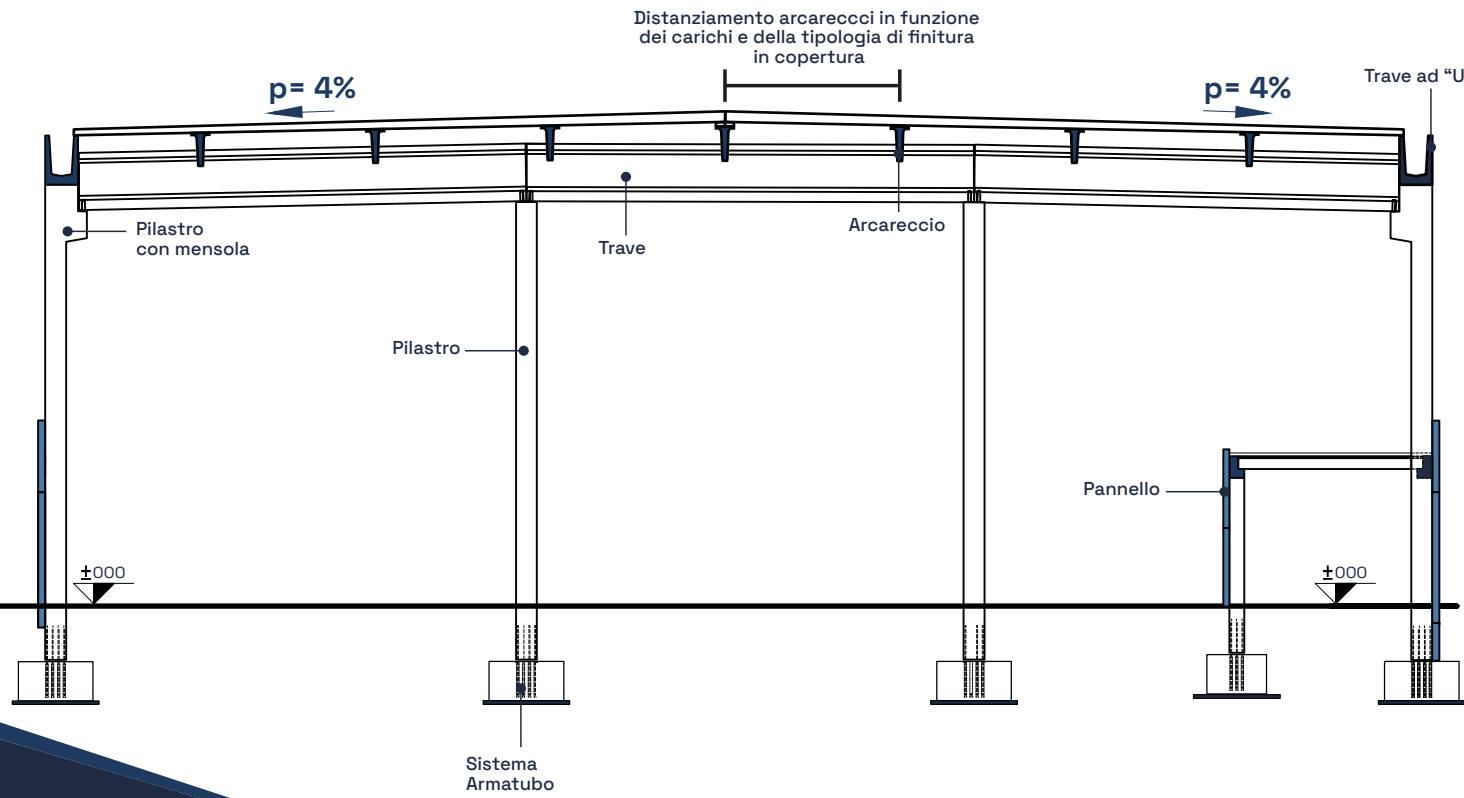

SOLUZIONE COPERTURA BACACIER

GEOMETRIA E PRESTAZIONI


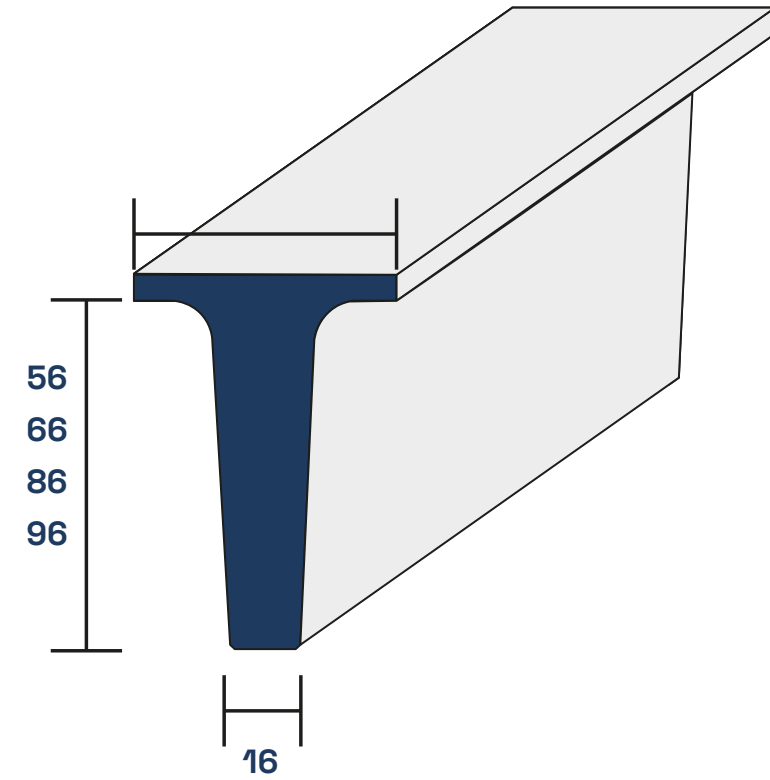


*Misure indicate in CM


SOLUZIONI

OGNI CONFIGURAZIONE, UNA RISPOSTA


SEZIONE TRASVERSALE ARcareccio

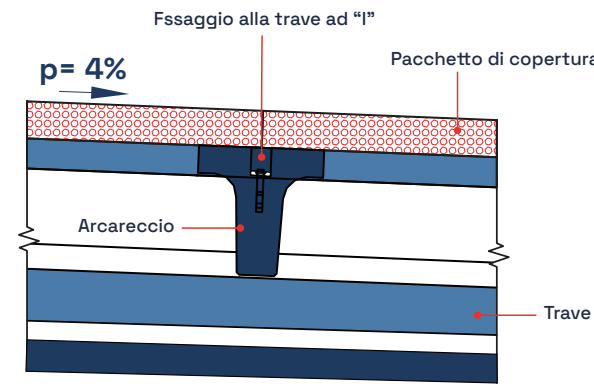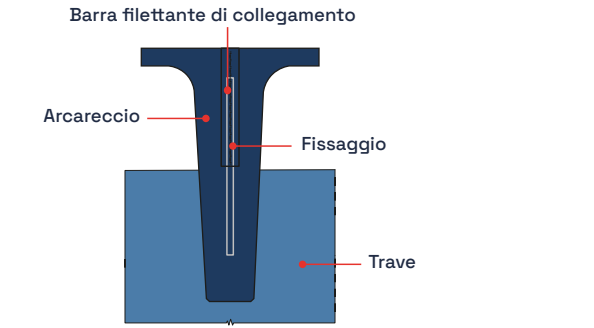


VISTA LATERALE

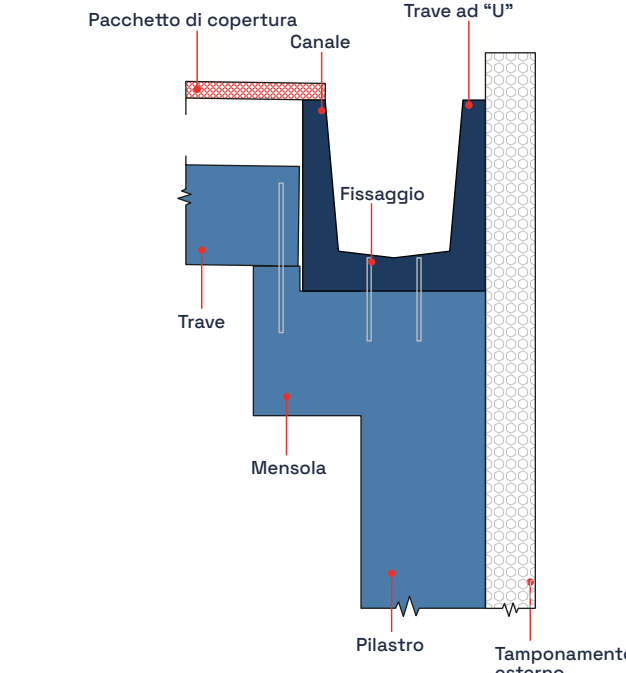


SEZIONE TRASVERSALE

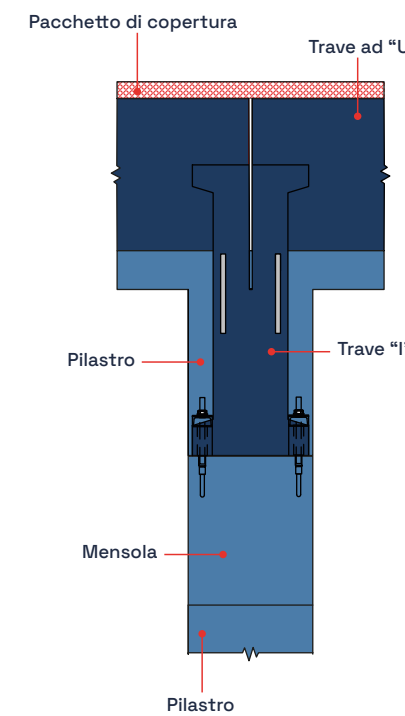

SEZIONE LONGITUDINALE FISSAGGIO TRAVI LATERALI

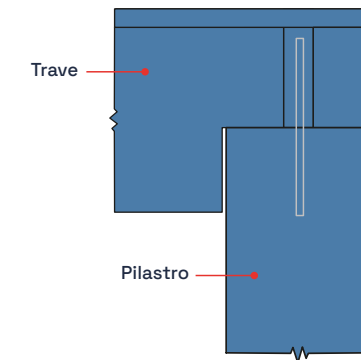


SEZIONE LONGITUDINALE FISSAGGIO TRAVI CENTRALI

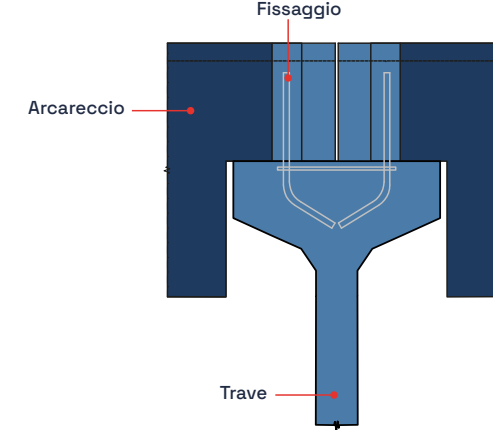


COMPONENTI DEL SISTEMA

GLI ELEMENTI DEL SISTEMA

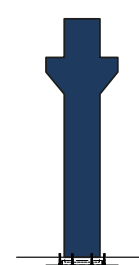



PILASTRO CON ARMATUBO

Pilastri di adeguate dimensioni con mensola per appoggio travi. Possibilità di implementazione con sistema armatubo.

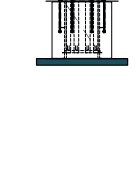


TRAVI A "I"

Elementi precompressi per impieghi centrali, con possibilità di appoggi speciali per scomparsa mensola.

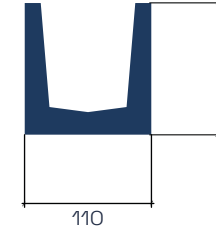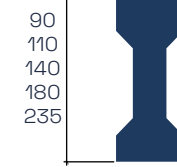


TRAVI A "U"

Elemento con ampio invaso per la raccolta delle acque meteorologiche su grandi superfici.

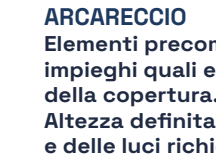

ARcareccio
Elementi precompressi di altezza variabile per impieghi quali elementi portanti secondari della copertura.
Altezza definita in funzione dei sovraccarichi e delle luci richieste.

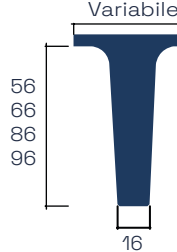

APPLICAZIONE E UTILIZZI

CONTESTI DI UTILIZZO



DETTAGLIO

NODO TRAVE-ARcareccio



Dove la forma prende volume

VANTAGGI

- ☀️ Compatibile con fotovoltaico e lucernari
- ≡ Numero ridotto di pilastri interni
- ↔️ Grandi luci libere
- 💧 Resistenza al fuoco R60'– R90'– R120'– R180'
- 📶 Nodi e vincoli sismici certificati

DATI TECNICI PRINCIPALI COPERTURA BACACIER

ALTEZZA TRAVE "I"	90 110 140 180 235 cm
ALTEZZA ARcareccio	56 66 86 96 cm
PENDENZA COPERTURA	4%
NODI SISMICI	Certificati
RESISTENZA AL FUOCO	Da R60' R90' a R120' estendibile fino R180'
MAGLIA STRUTTURALE	A seconda della necessità

*Compatibile con impianti fotovoltaici, evacuatori di fumo e calore (EFC) e sistemi antincendio Spinkler